




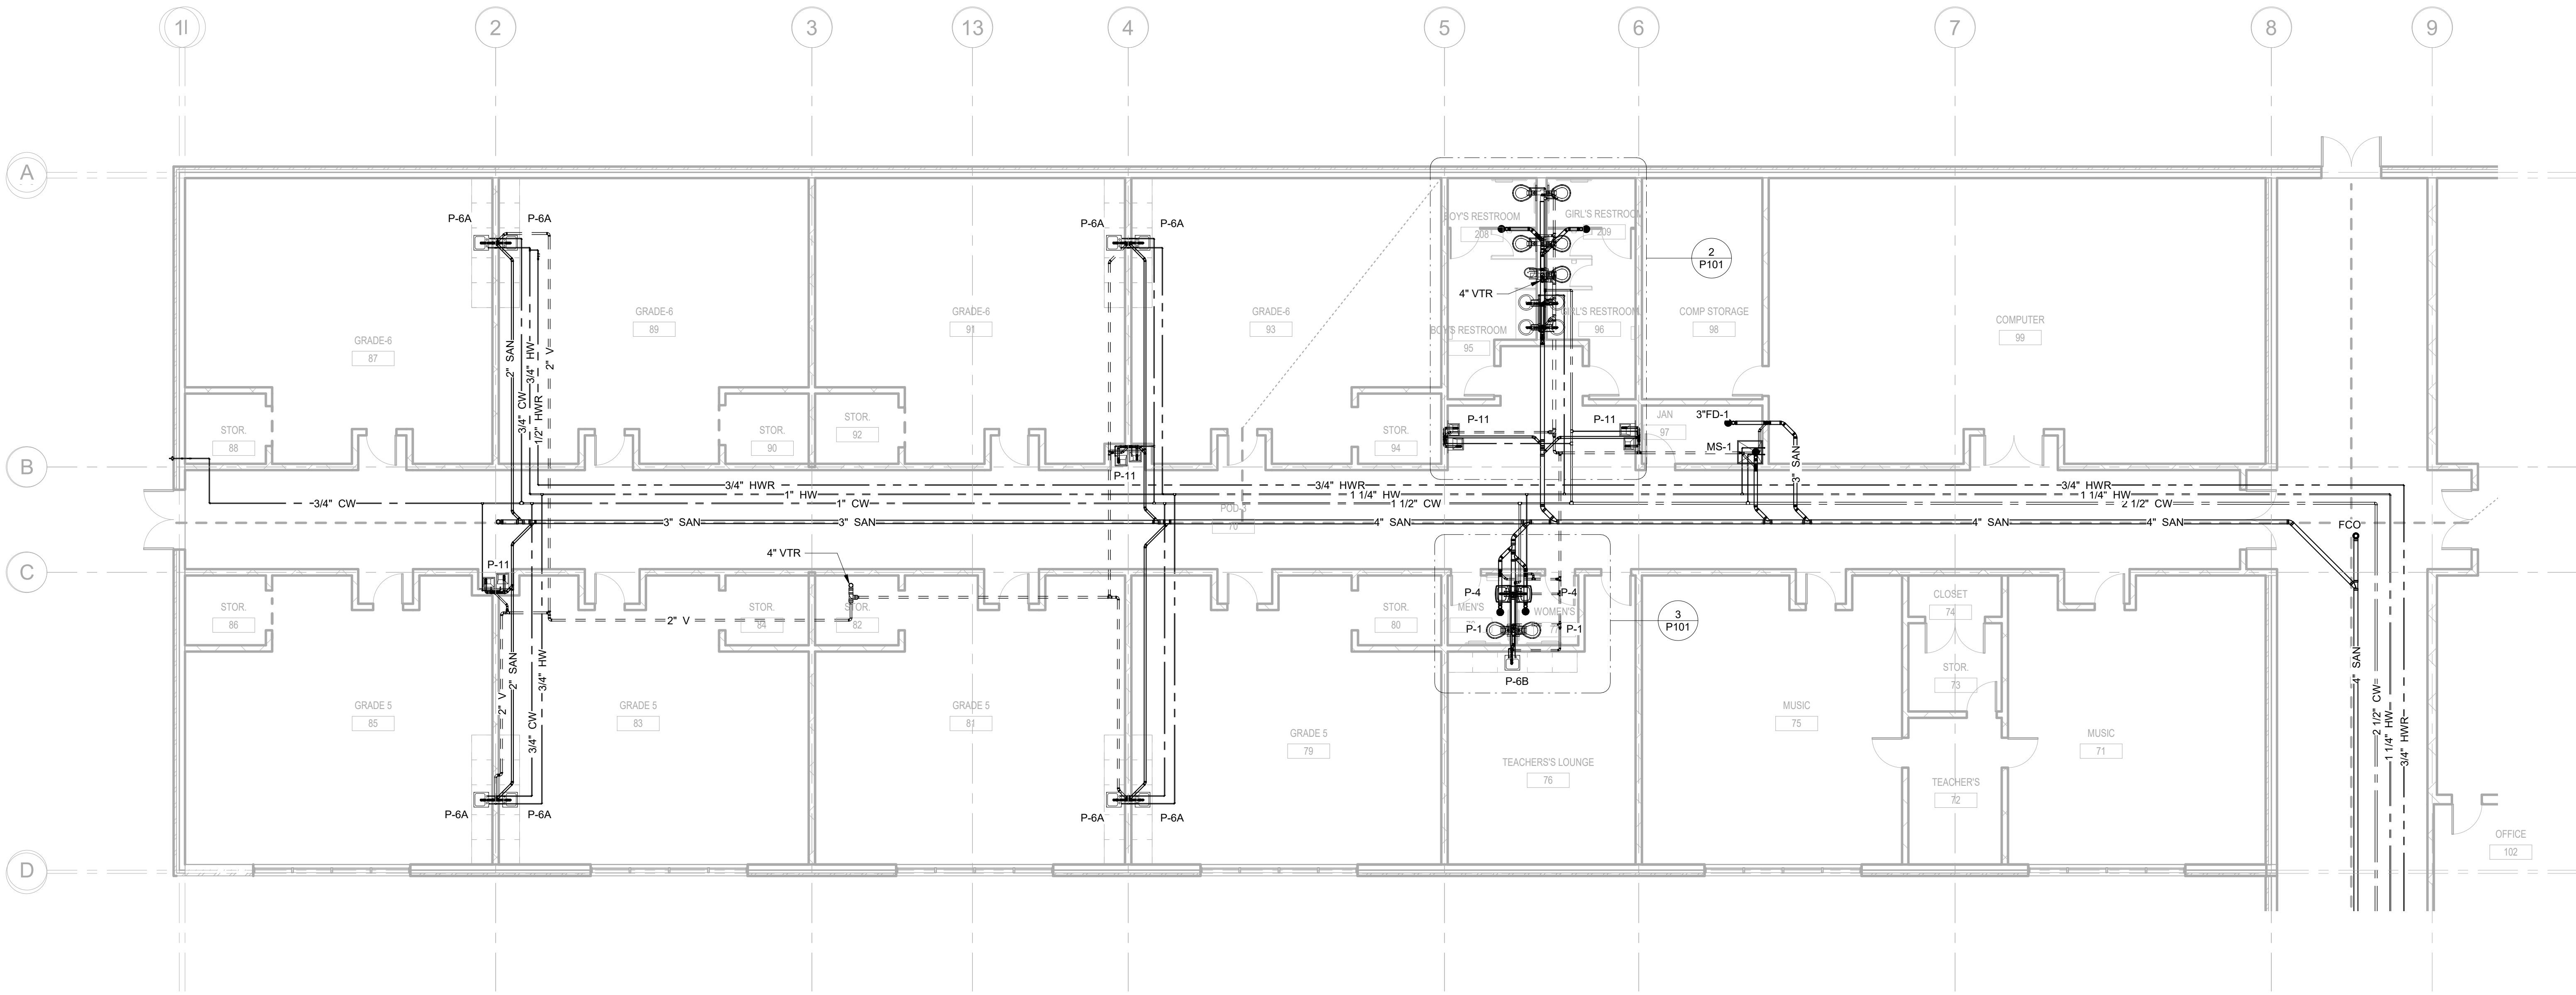

1 FIRST FLOOR - SANITARY - WATER & GAS - AREA A
1/8" = 1'-0"

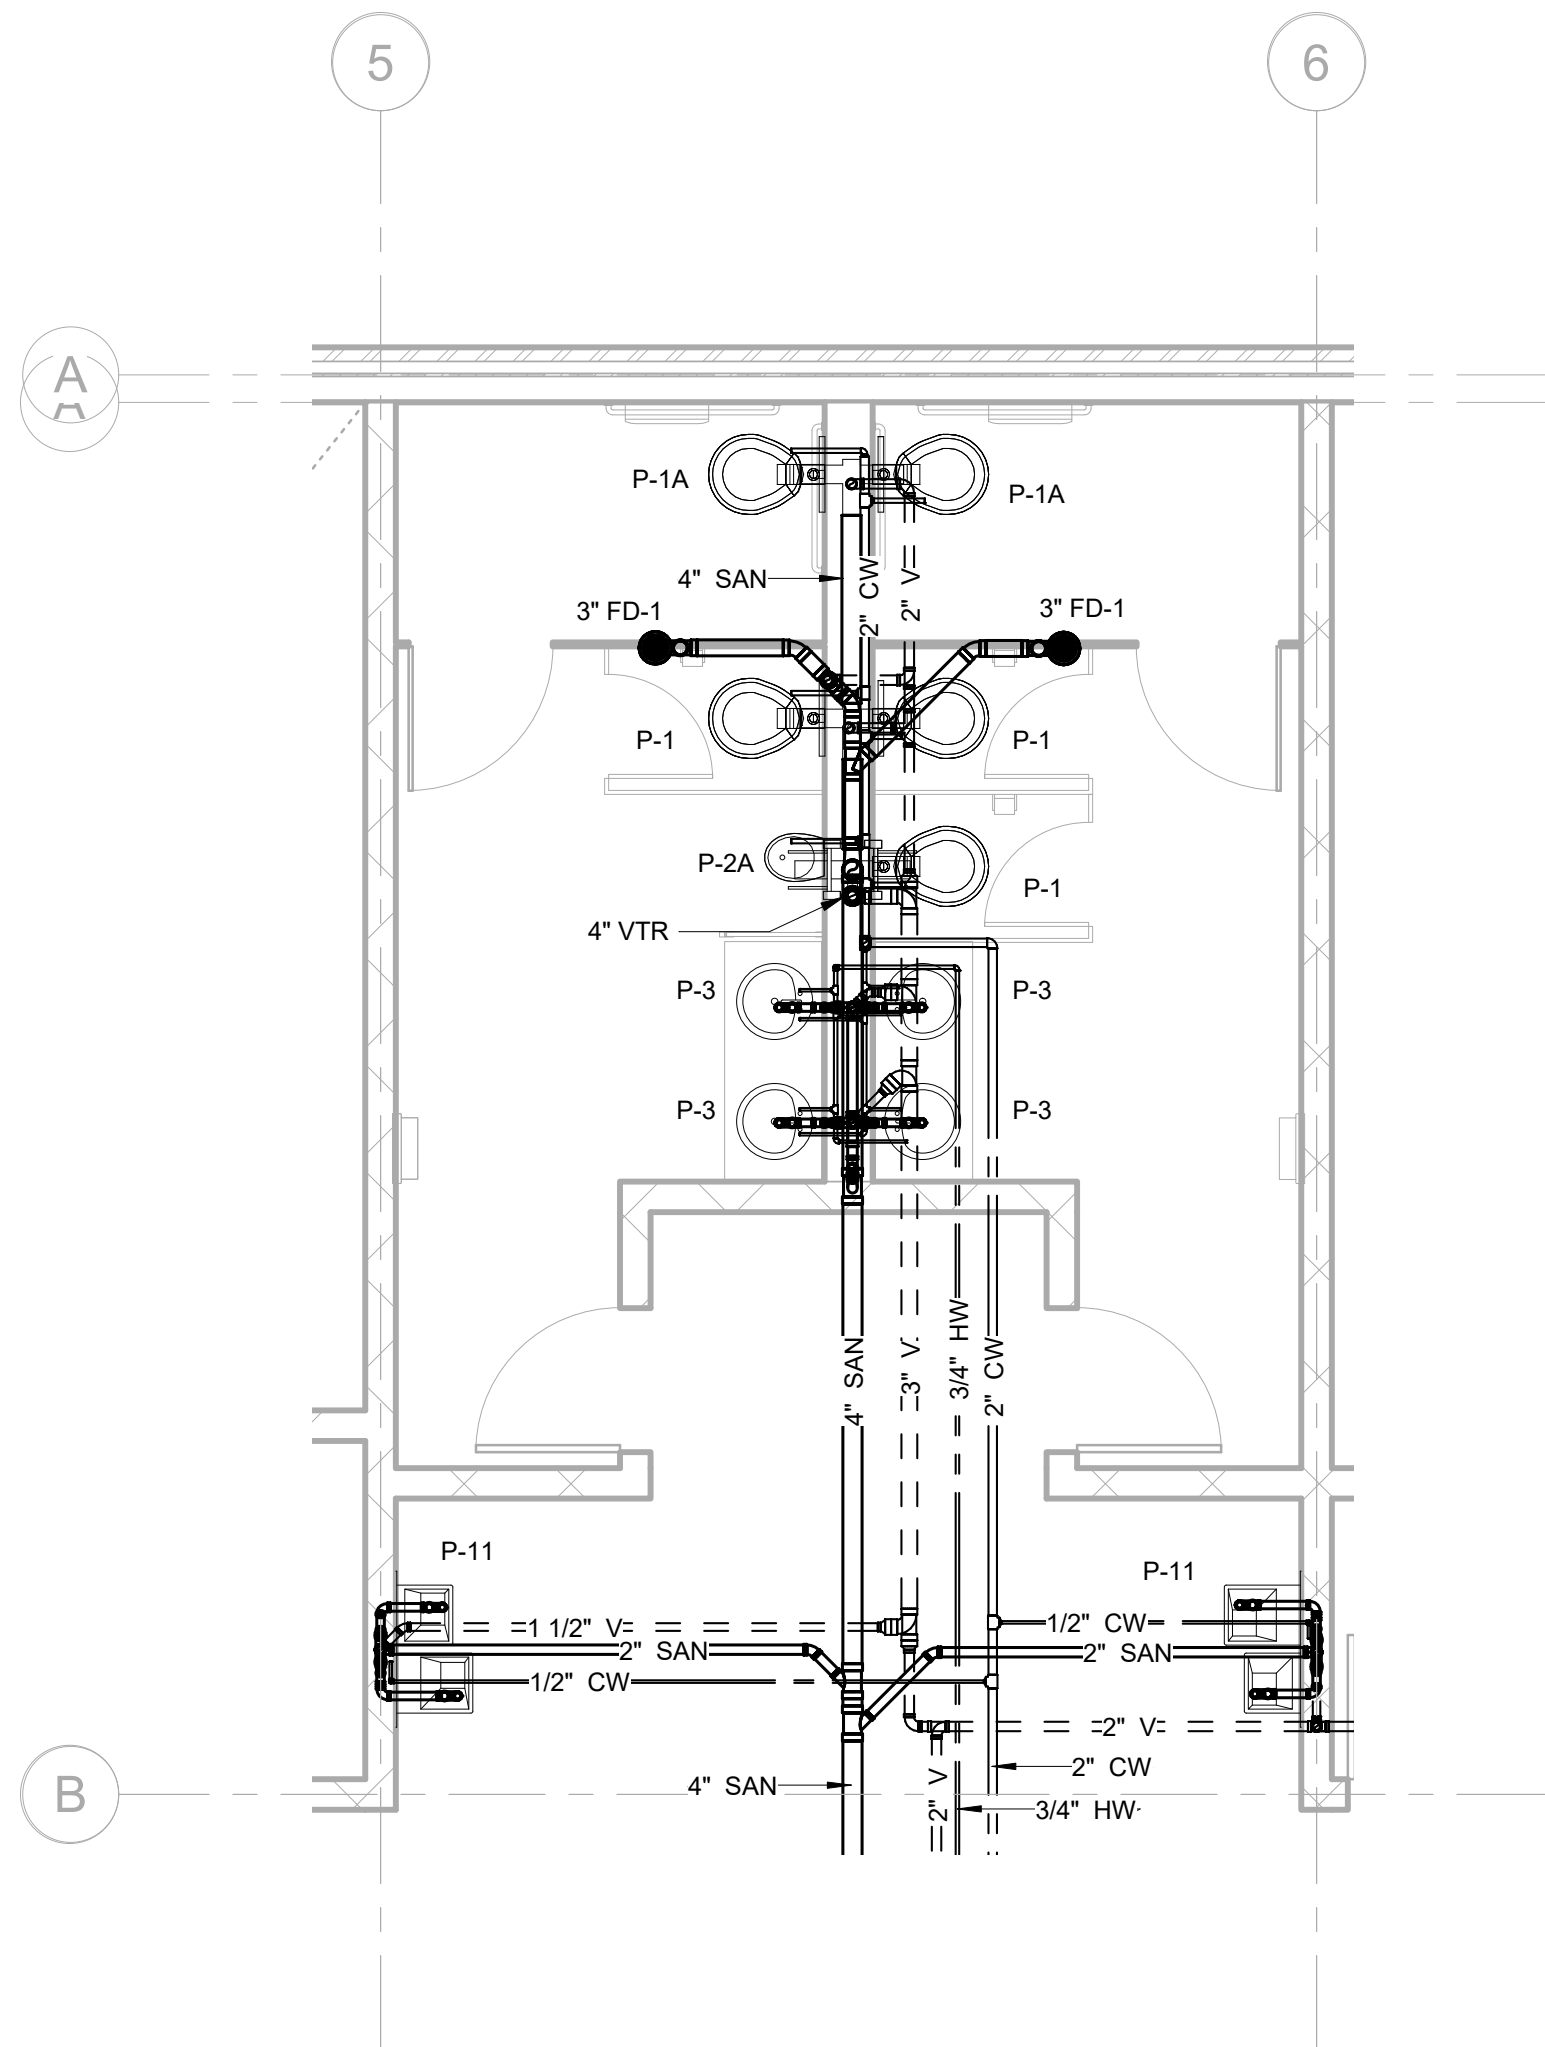

2 FIRST FLOOR - AREA A - BOYS & GIRLS RESTROOM
1/4" = 1'-0"

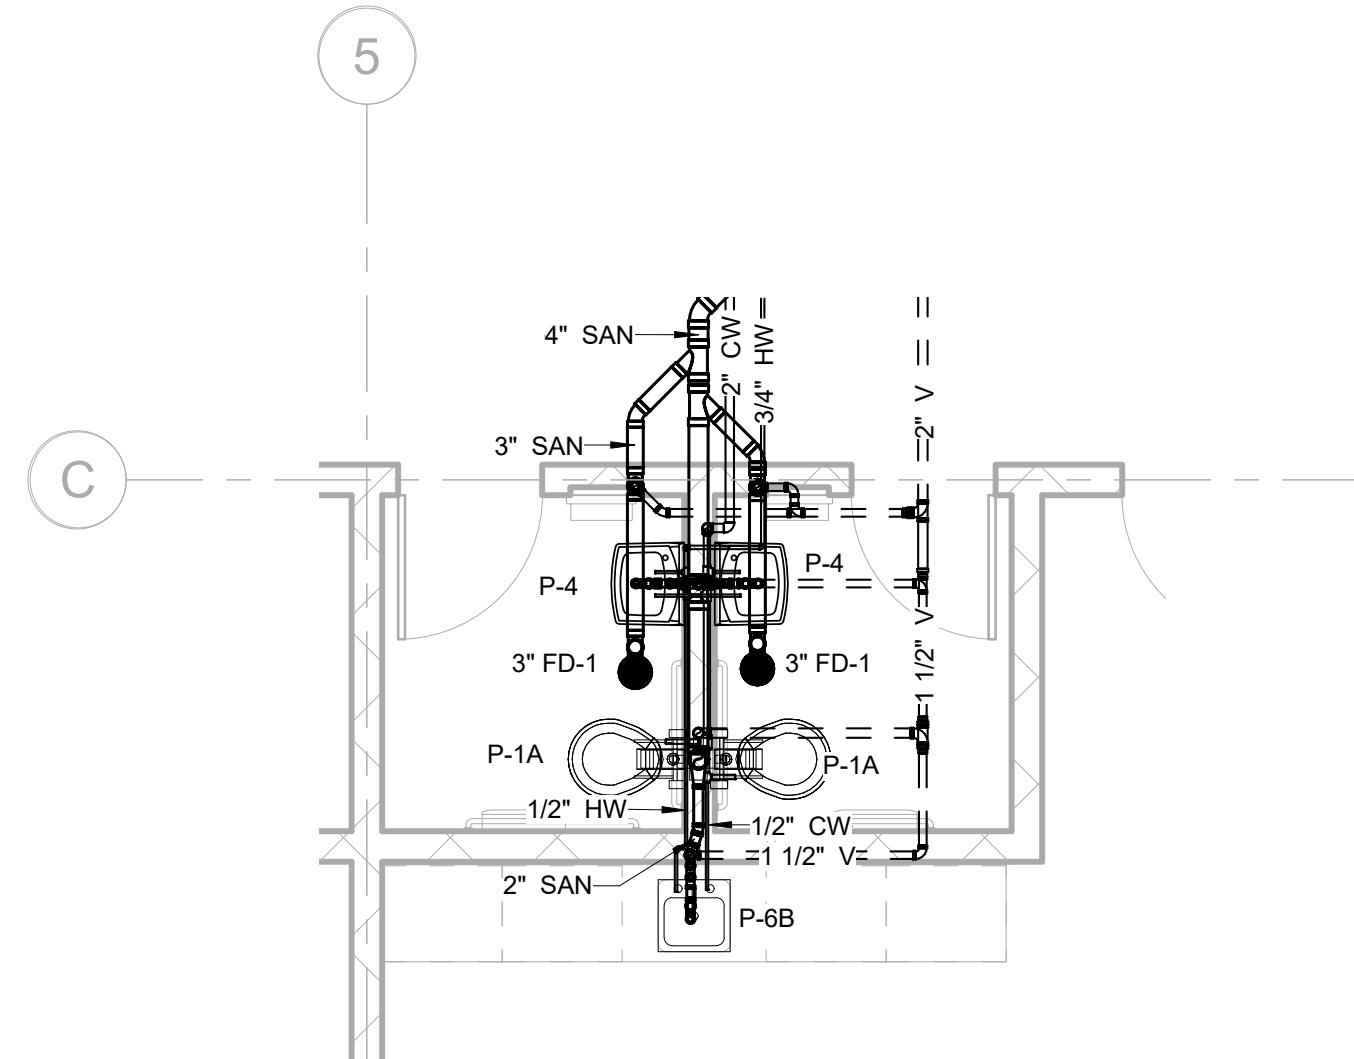

3 FIRST FLOOR - AREA A - MEN'S & WOMEN'S RESTROOM
1/4" = 1'-0"

GENERAL NOTES

- REFER TO P001 FOR GENERAL NOTES, SYMBOL LEGEND AND LIST OF ABBREVIATIONS.

ARCHITECT

MEP. ENG.

NIST

FOR OFFICIAL USE ONLY

U.S. DEPARTMENT OF COMMERCE

OFFICE OF FACILITIES & PROPERTY MANAGEMENT

NIST - PRIMARY SCHOOL

PLUMBING FLOOR PLAN AREA A

P101

DWG. P101

SH. NO. OF

08/15/2022 Project Number

VAY DATE PROJECT LEADER

DATE FACILITIES ENGR. OFF.

DATE SHED - NIST FIRE MARSHAL/AHJ


DATE SAFETY

DATE ENVIRONMENTAL MANAGEMENT


DATE MAINTENANCE ENG. OFF.

DATE SPONSOR


APPROVED BY

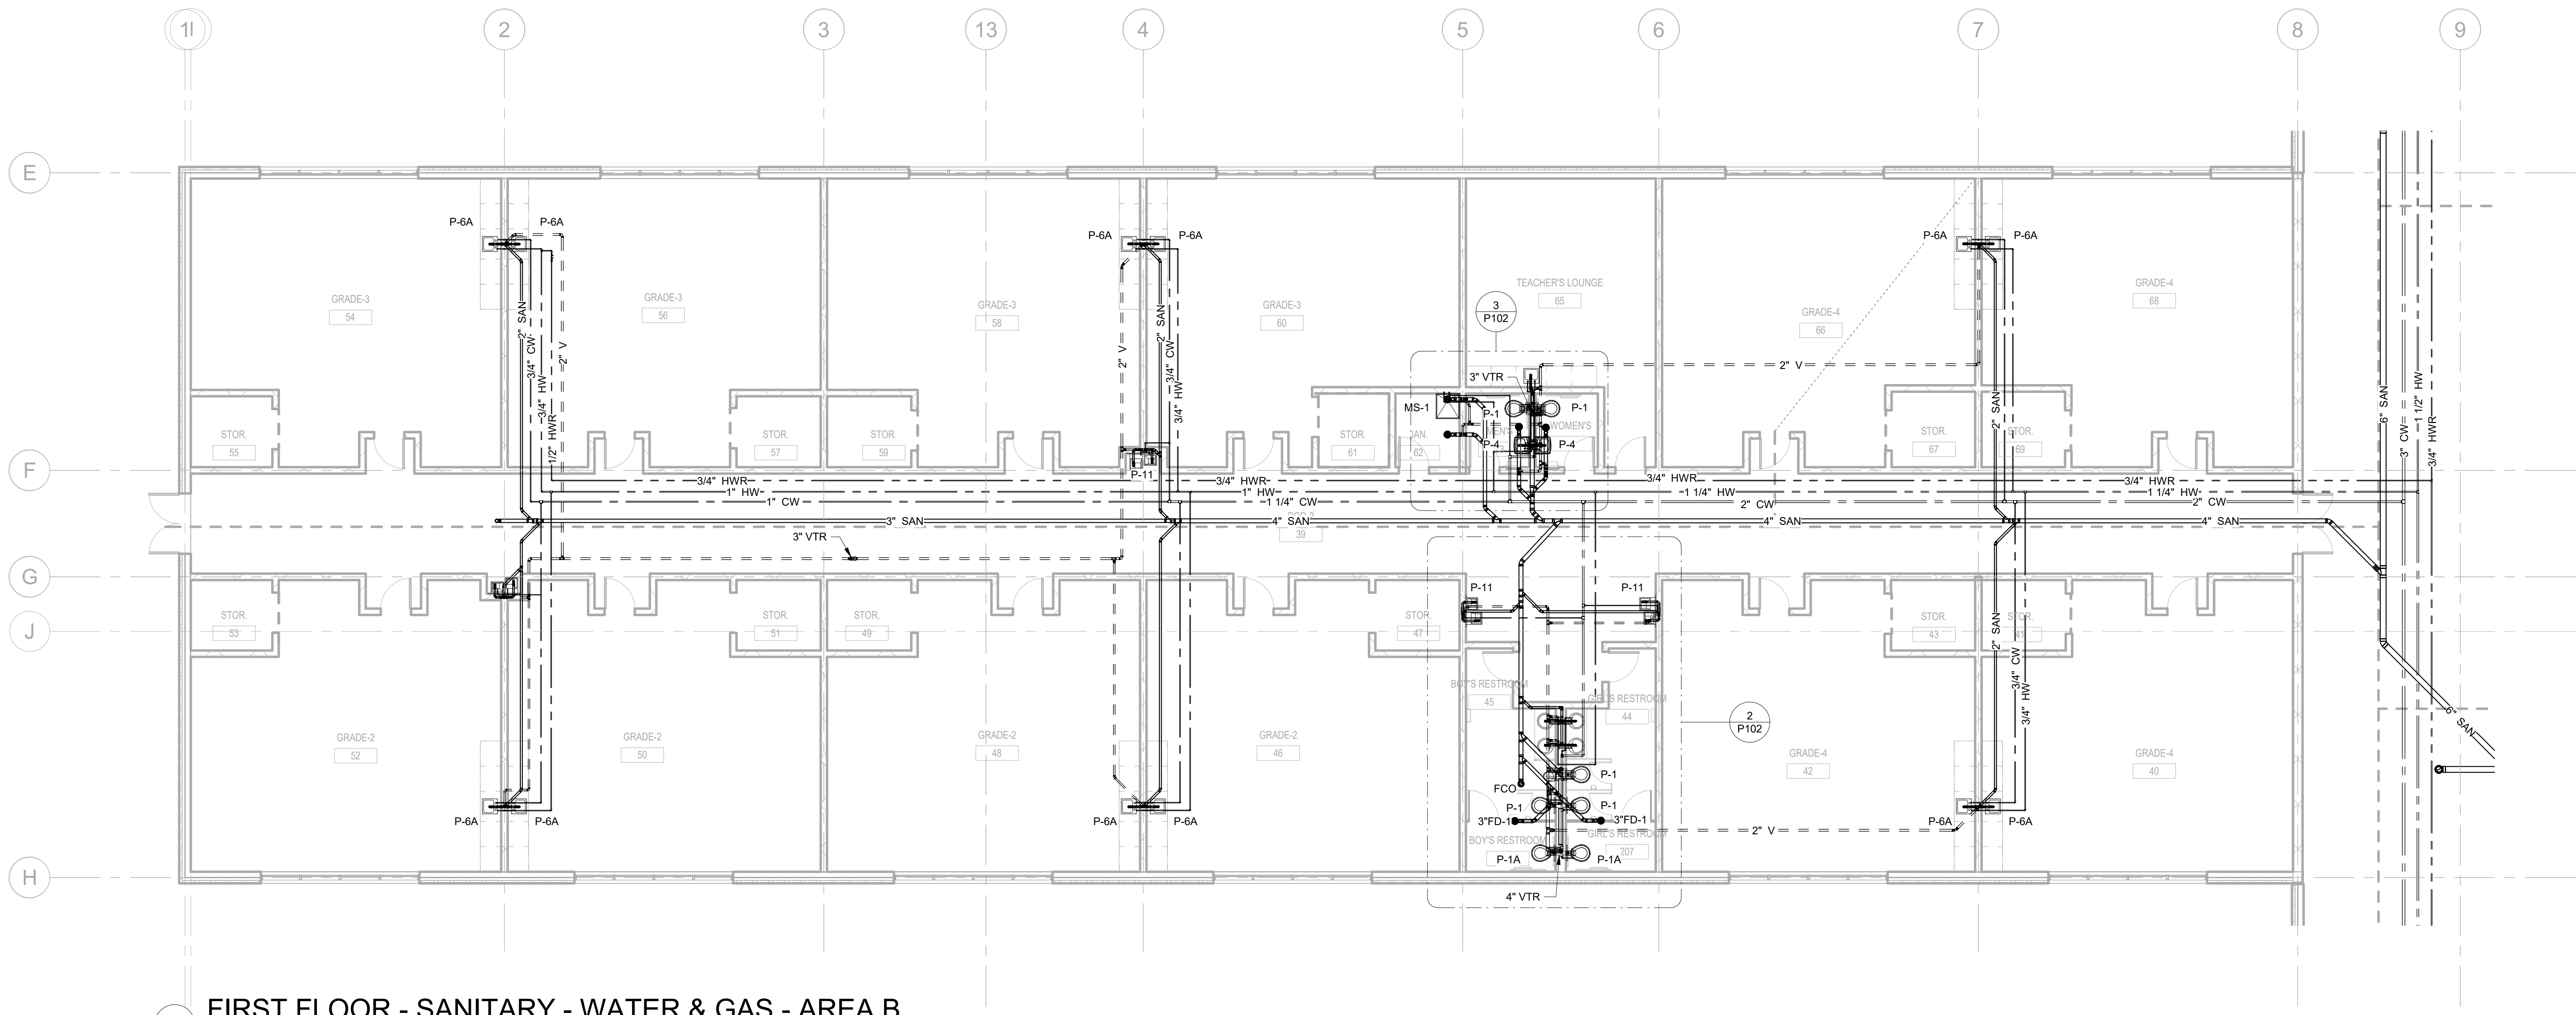

1 FIRST FLOOR - SANITARY - WATER & GAS - AREA B
1/8" = 1'-0"

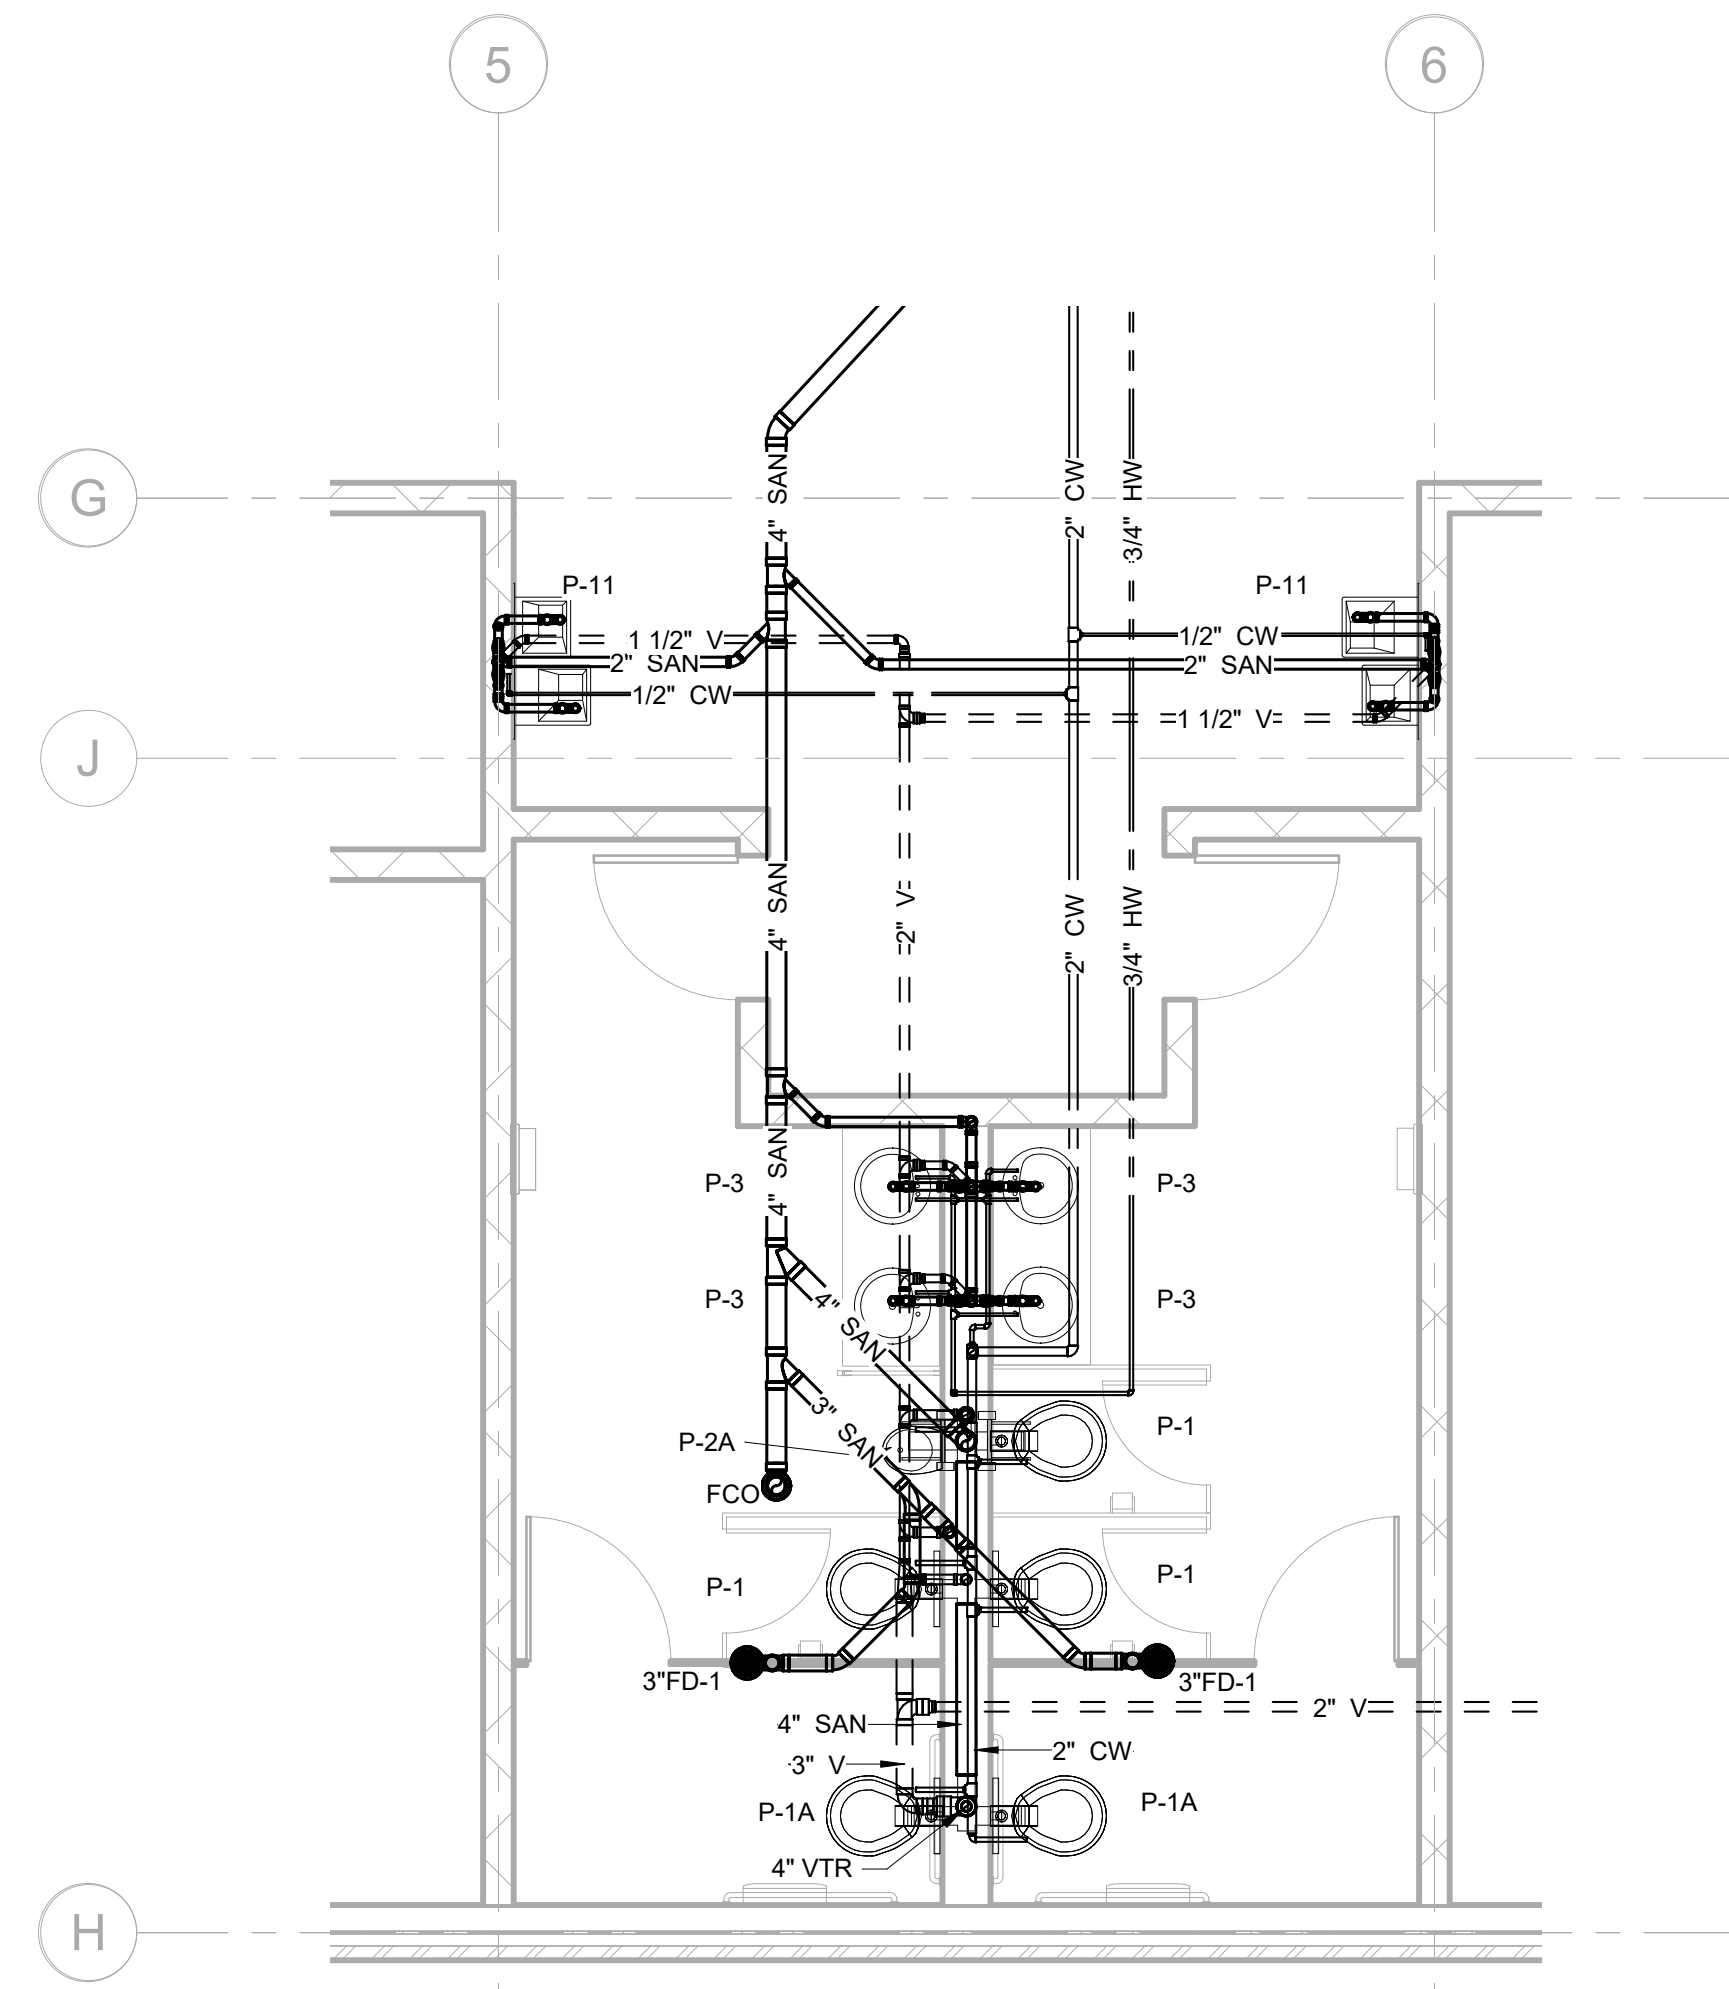


2 FIRST FLOOR - AREA B - BOYS & GIRLS RESTROOM
1/4" = 1'-0"

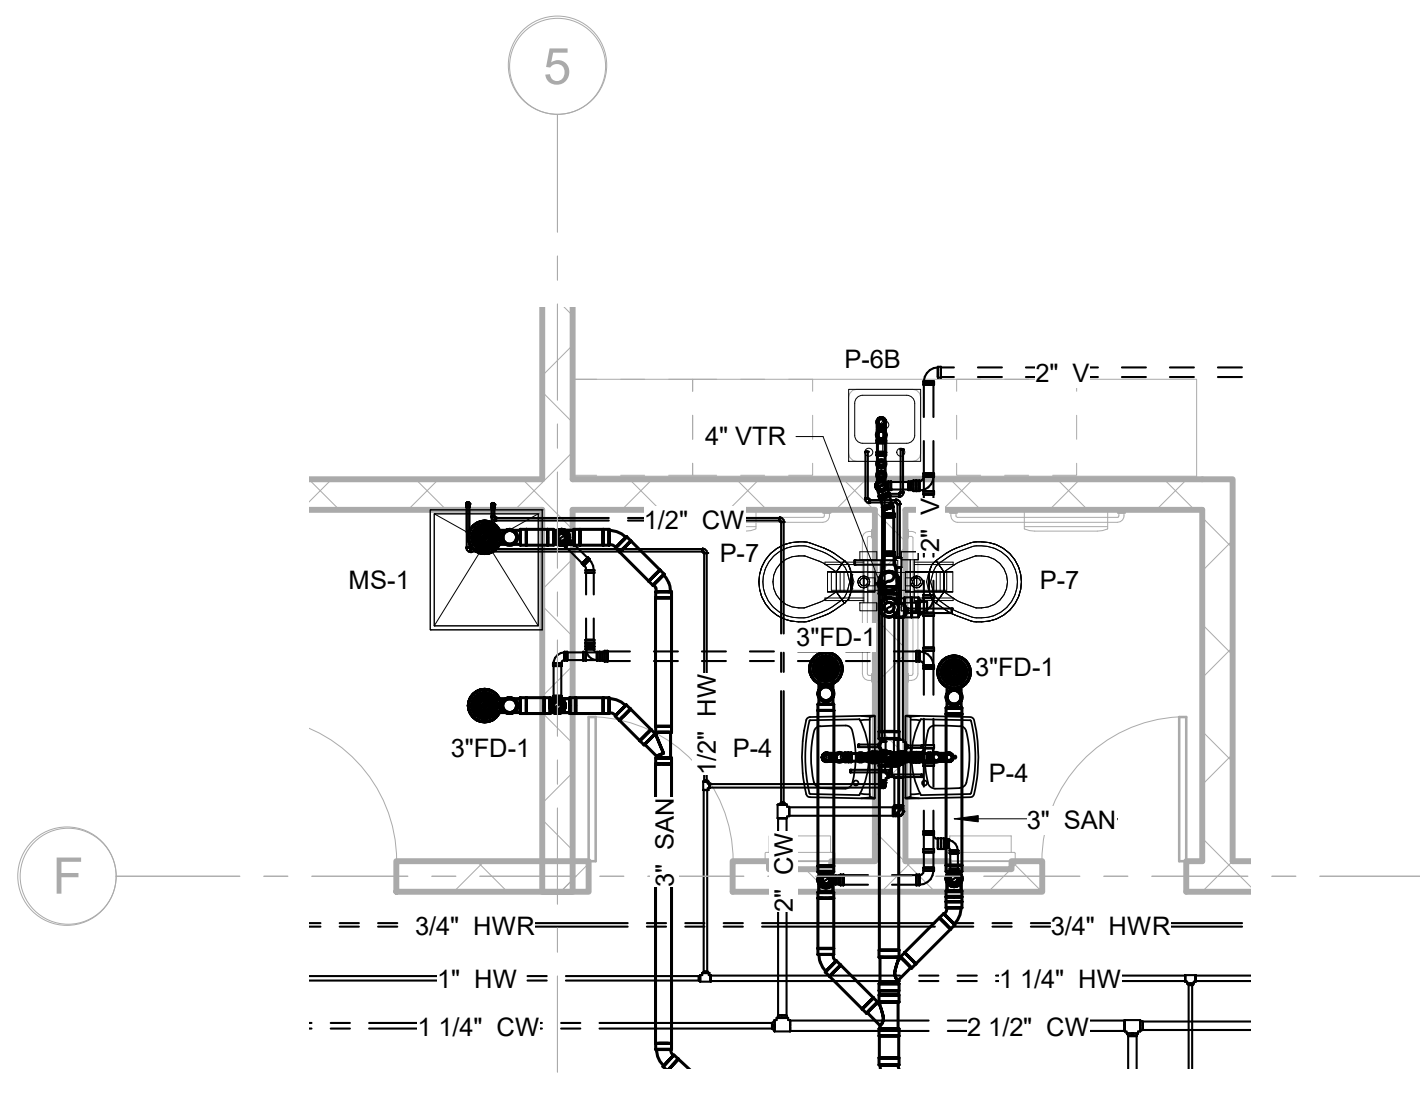


3 FIRST FLOOR - AREA B - MEN'S & WOMEN'S RESTROOM
1/4" = 1'-0"

REVISION	DESCRIPTION	BY	DATE
GENERAL NOTES 1. REFER TO P001 FOR GENERAL NOTES, SYMBOL LEGEND AND LIST OF ABBREVIATIONS.			
		ARCHITECT	
		MEP. ENG.	
NIST FOR OFFICIAL USE ONLY U.S. DEPARTMENT OF COMMERCE OFFICE OF FACILITIES & PROPERTY MANAGEMENT NIST - PRIMARY SCHOOL PLUMBING FLOOR PLAN - AREA B P102 SH. NO. ____ OF ____ DWG. P102			

APPROVED BY: _____ DATE: _____ SPONSOR: _____ DATE: _____ MAINTENANCE ENG. OFF.: _____ DATE: _____ ENVIRONMENTAL MANAGEMENT: _____ DATE: _____ SAFETY: _____ DATE: _____ SHED - NIST FIRE MARSHAL/AHJ: _____ DATE: _____ FACILITIES ENGR. OFF.: _____ DATE: _____ VAY: _____ DATE: _____ AA: _____ DATE: _____ 08/15/2022 Project Number: _____ DATE: _____ PROJECT/ W.O. #: _____

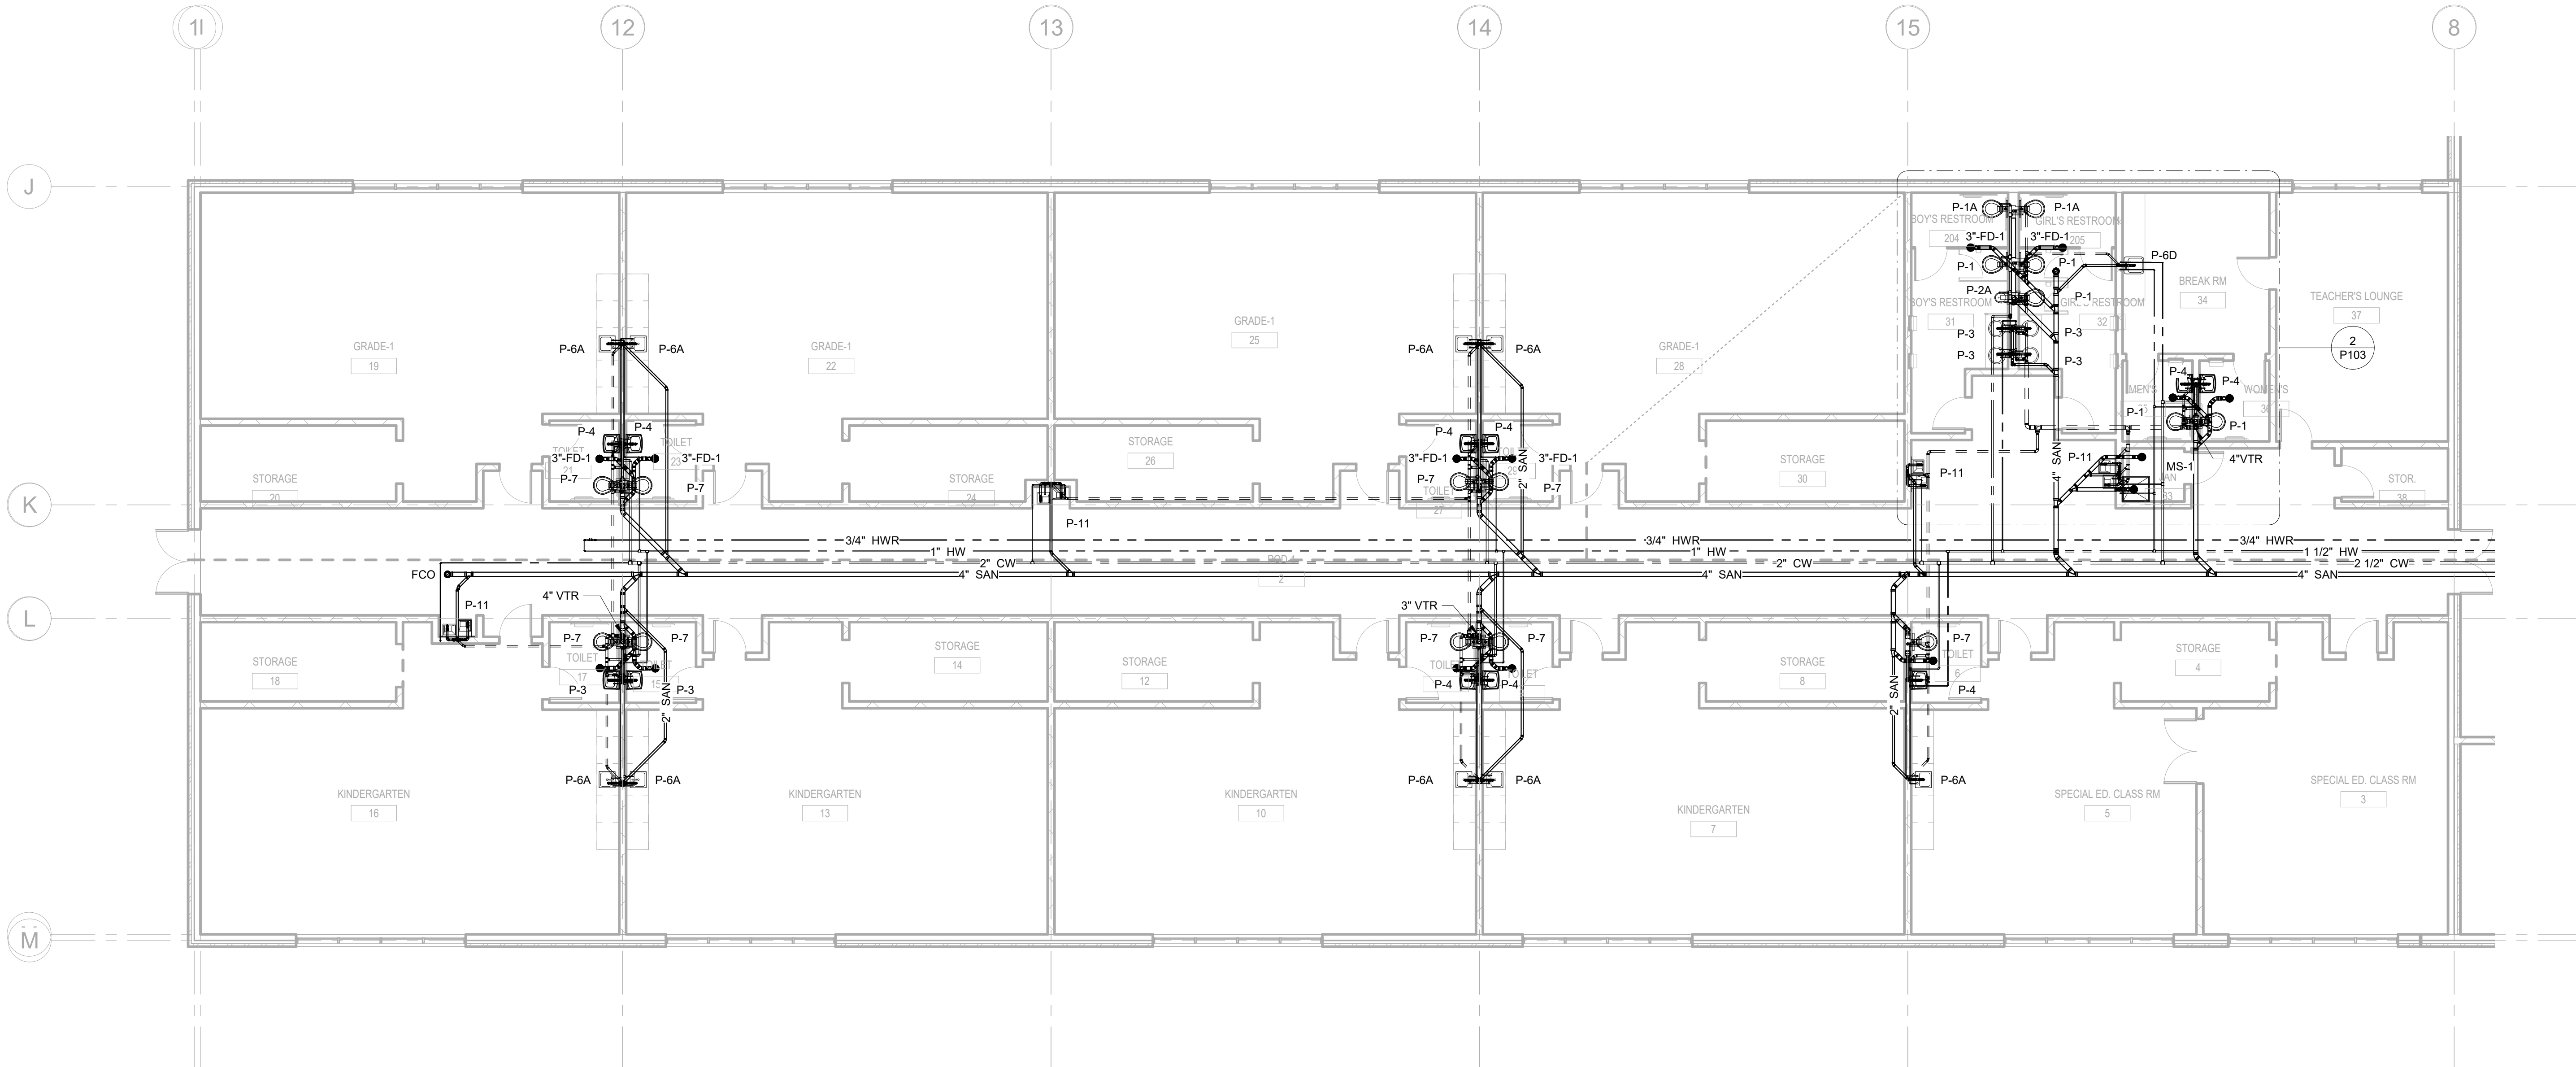

1 FIRST FLOOR - SANITARY - WATER & GAS - AREA C
1/8" = 1'-0"

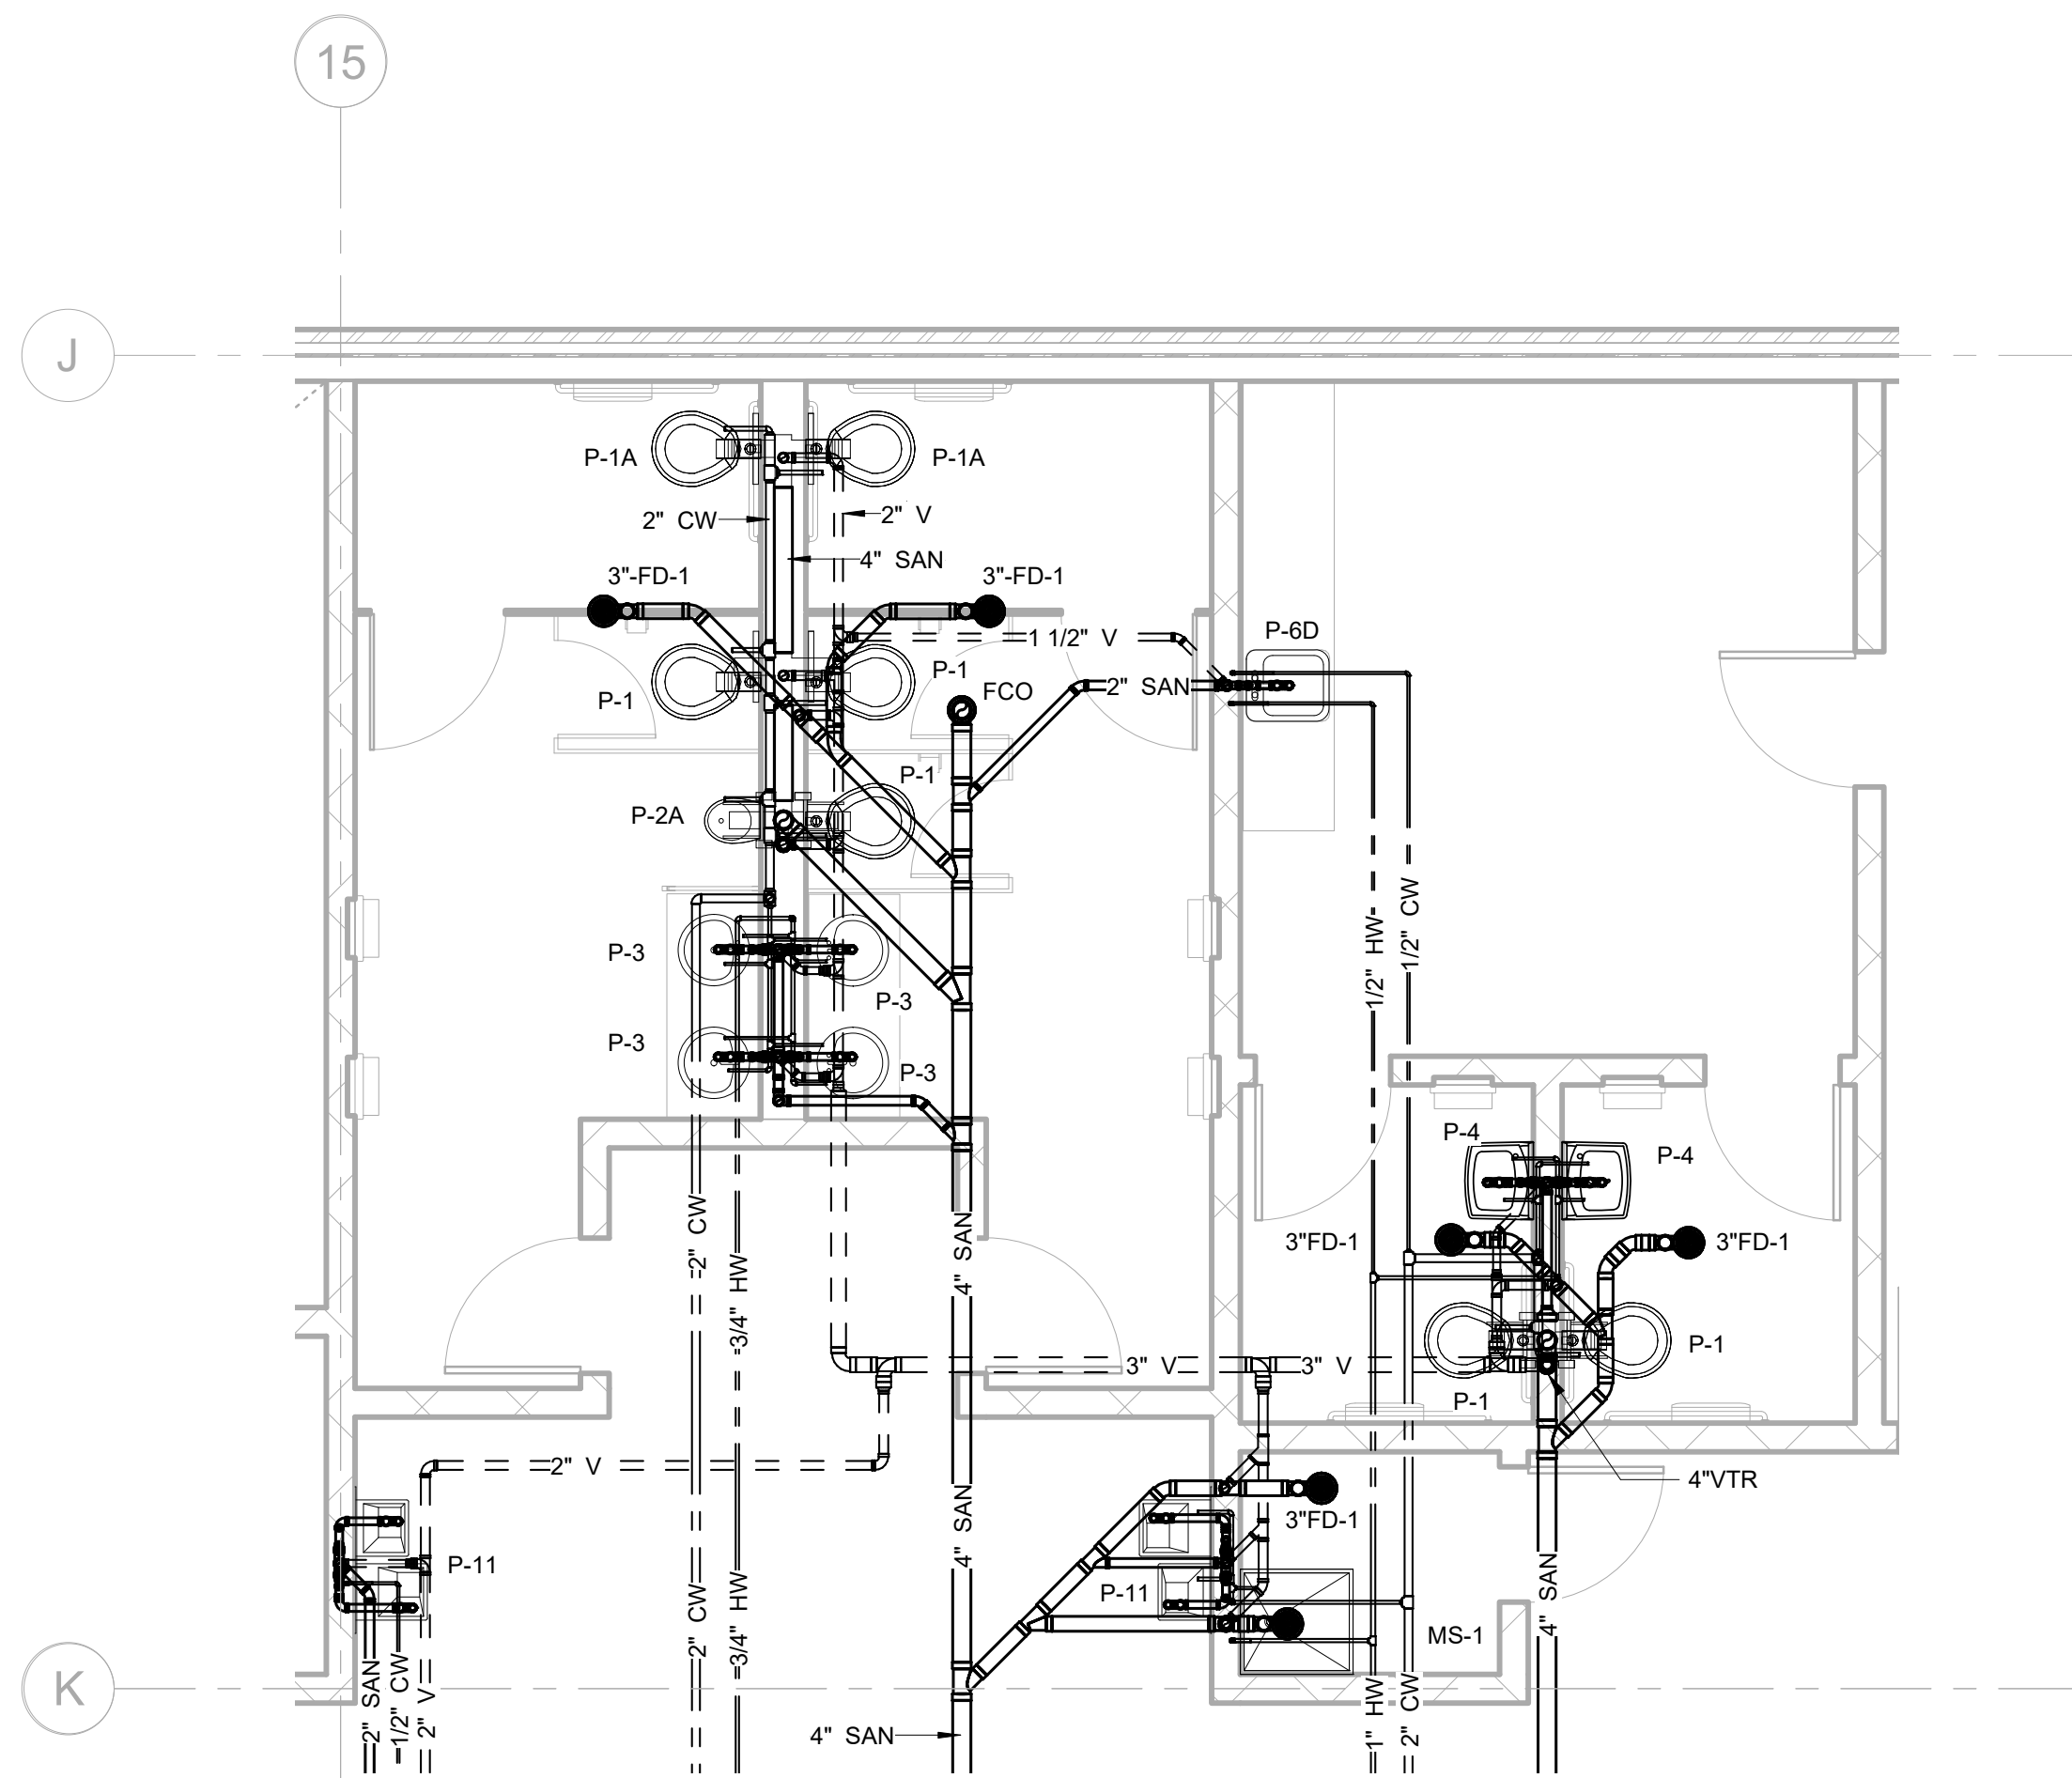

2 FIRST FLOOR - AREA C - BOYS & GIRLS MEN'S & WOMEN'S RESTROOM
1/4" = 1'-0"

GENERAL NOTES

1. REFER TO P001 FOR GENERAL NOTES, SYMBOL LEGEND AND LIST OF ABBREVIATIONS.

ARCHITECT

MEP. ENG.

NIST

FOR OFFICIAL USE ONLY

U.S. DEPARTMENT OF COMMERCE

OFFICE OF FACILITIES & PROPERTY MANAGEMENT

NIST - PRIMARY SCHOOL

PLUMBING FLOOR PLAN - AREA C

P103

DWG. P103

SH. NO. OF

08/15/2022 Project Number

VAY Project Leader

DATE FACILITIES ENGR. OFF.

DATE SHED - NIST FIRE MARSHAL/AHJ


DATE SAFETY

DATE ENVIRONMENTAL MANAGEMENT

DATE MAINTENANCE ENG. OFF.

DATE SPONSOR

APPROVED BY

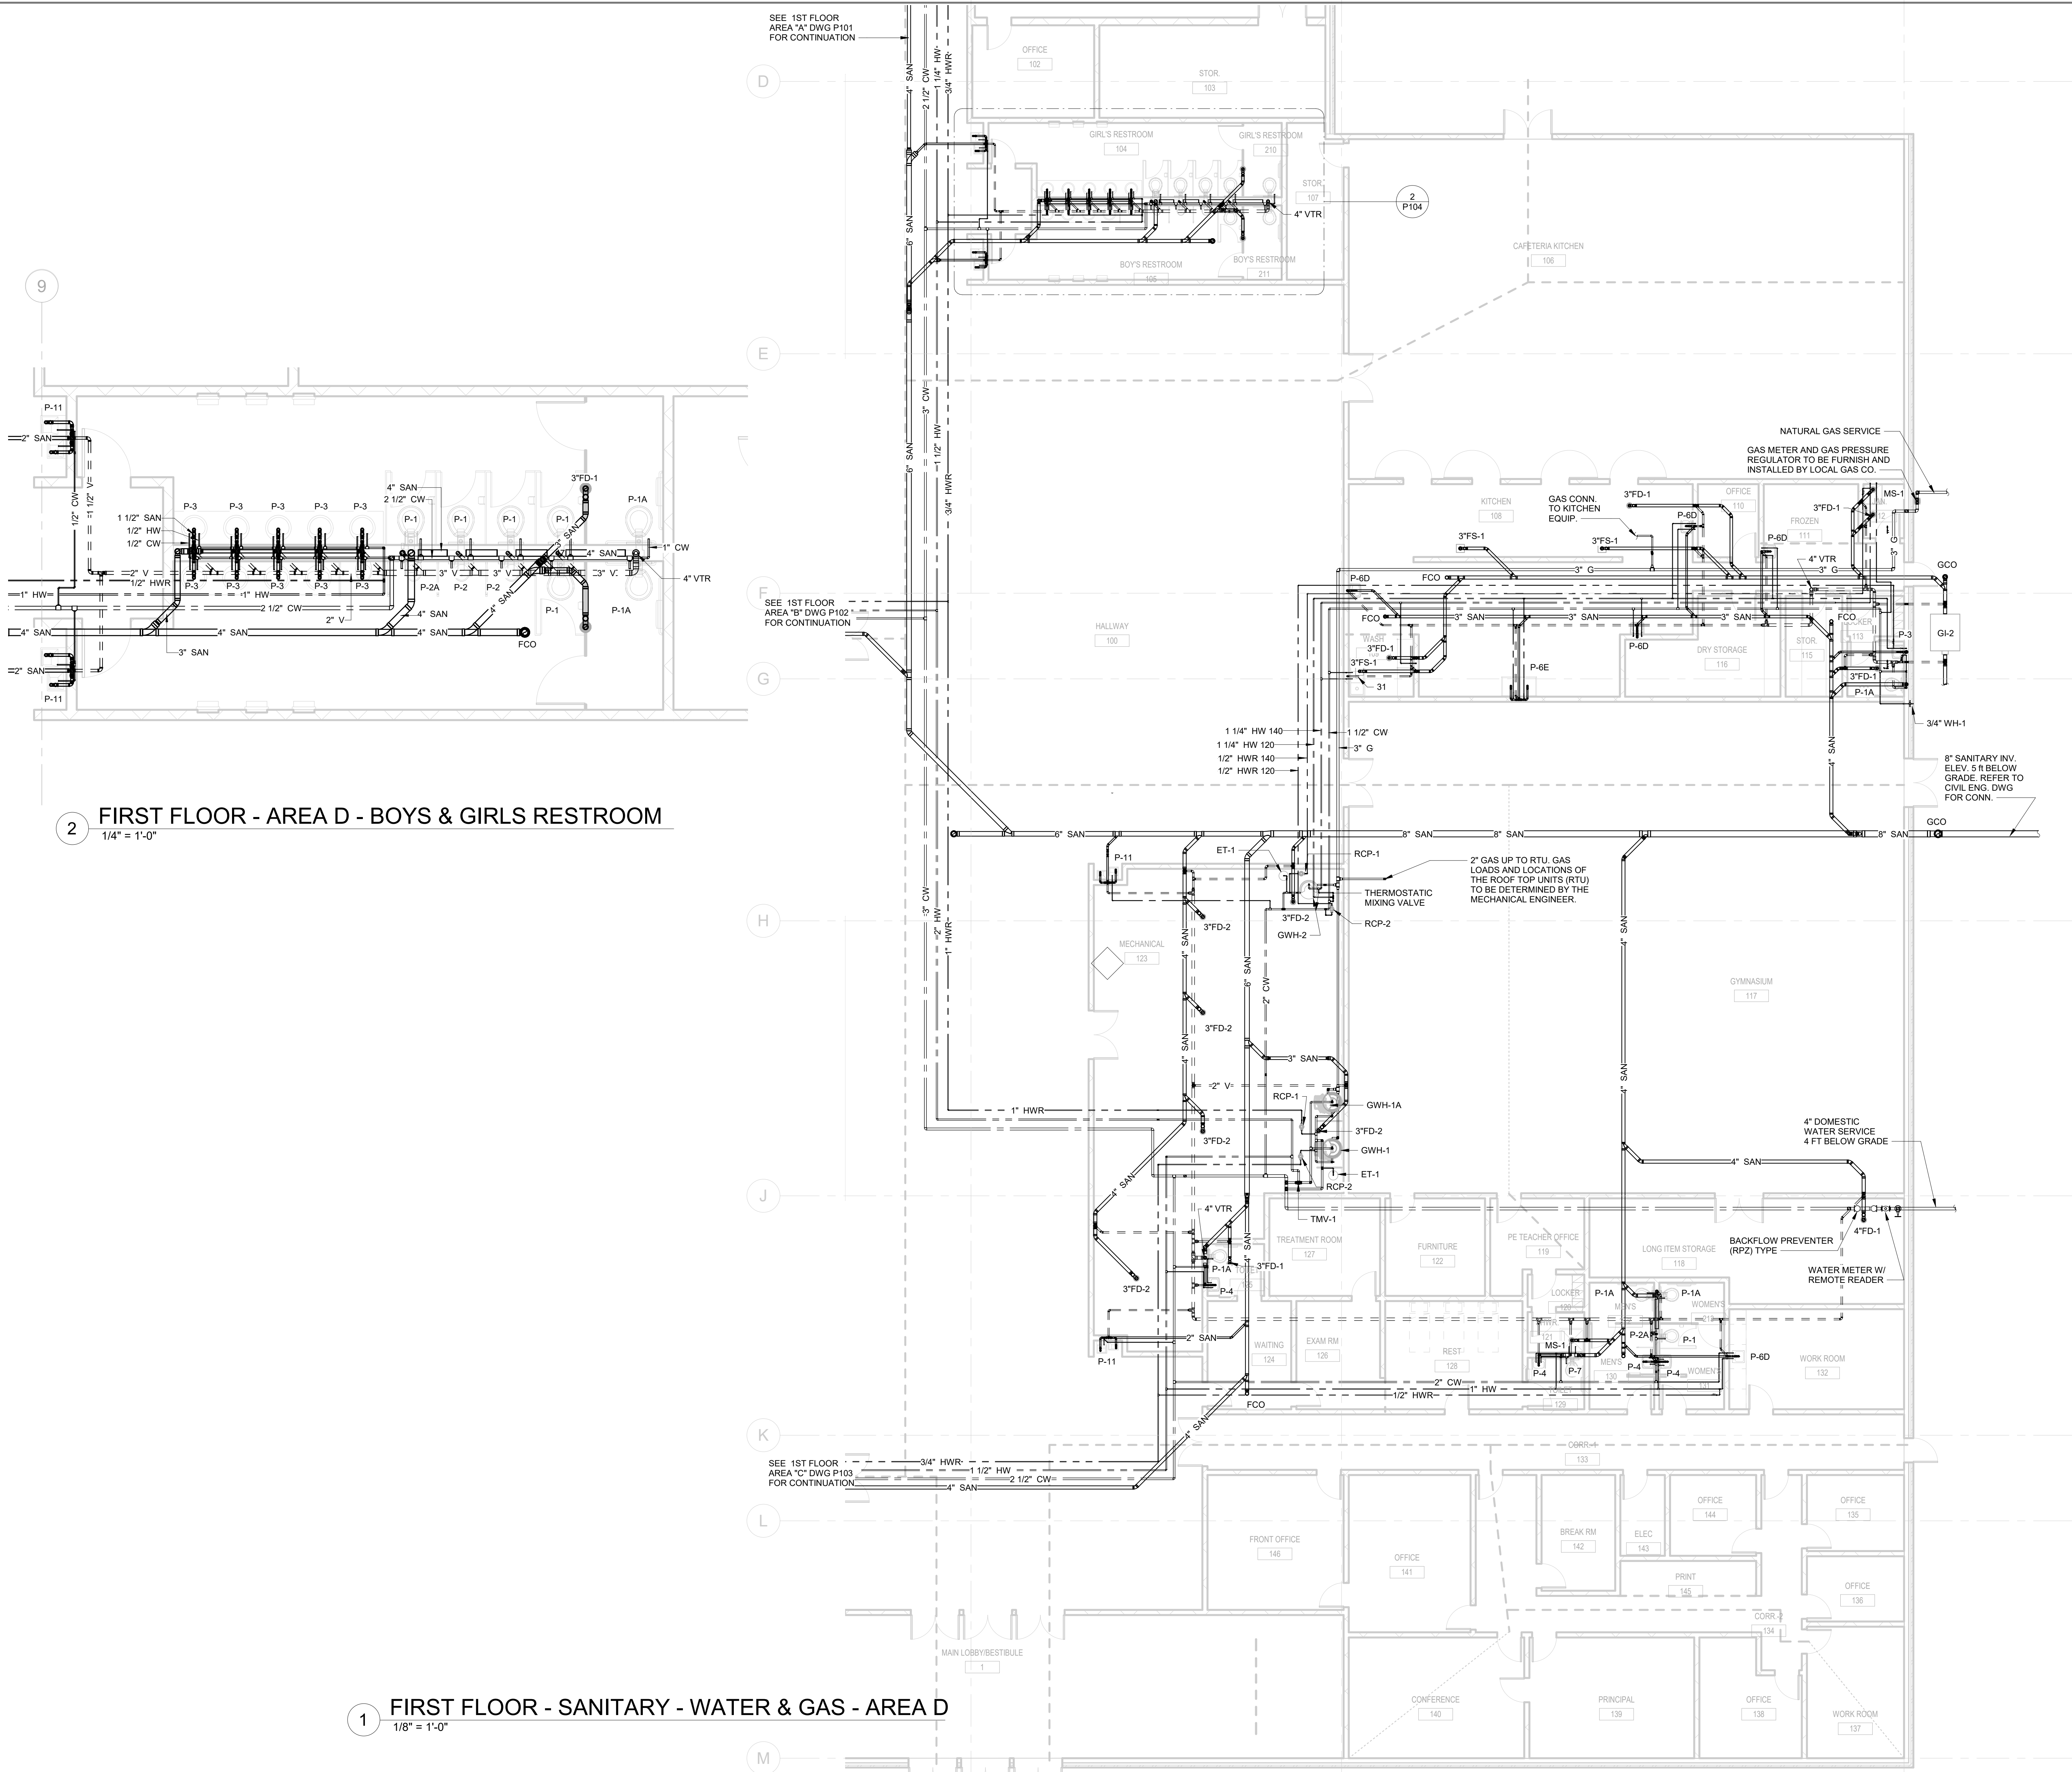

2 FIRST FLOOR - AREA D - BOYS & GIRLS RESTROOM
1/4" = 1'-0"

1 FIRST FLOOR - SANITARY - WATER & GAS - AREA D
1/8" = 1'-0"

GENERAL NOTES

1. REFER TO P001 FOR GENERAL NOTES, SYMBOL LEGEND AND LIST OF ABBREVIATIONS.

ARCHITECT

MEP. ENG.

NIST

FOR OFFICIAL USE ONLY

U.S. DEPARTMENT OF COMMERCE

OFFICE OF FACILITIES & PROPERTY MANAGEMENT

NIST - PRIMARY SCHOOL

PLUMBING FLOOR PLAN - AREA D

P104

DWG. P104

SH. NO. OF

08/15/2022 Project Number

AA DRAWN BY

VAY PROJECT LEADER

FACILITIES ENGR. OFF.

SHED - NIST FIRE MARSHAL/AHJ

SAFETY

ENVIRONMENTAL MANAGEMENT

MAINTENANCE ENG. OFF.

SPONSOR

APPROVED BY