
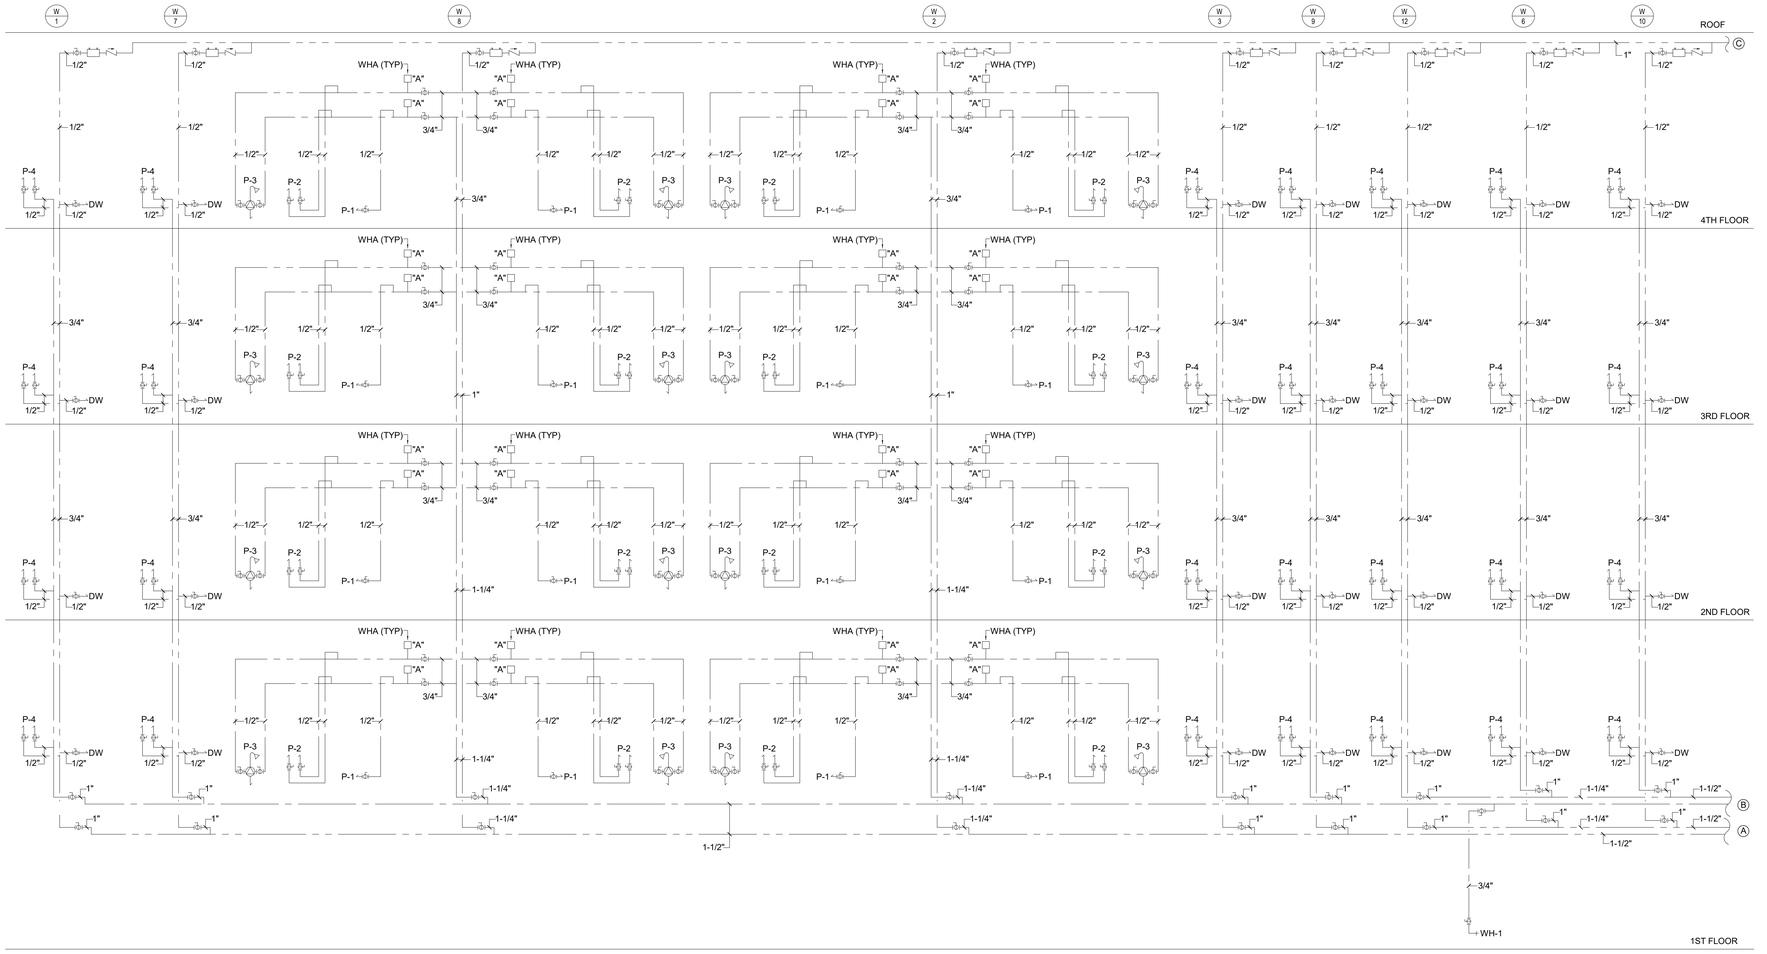


1 APARTMENT BLDG - WATER RISER DIAGRAM

NTS

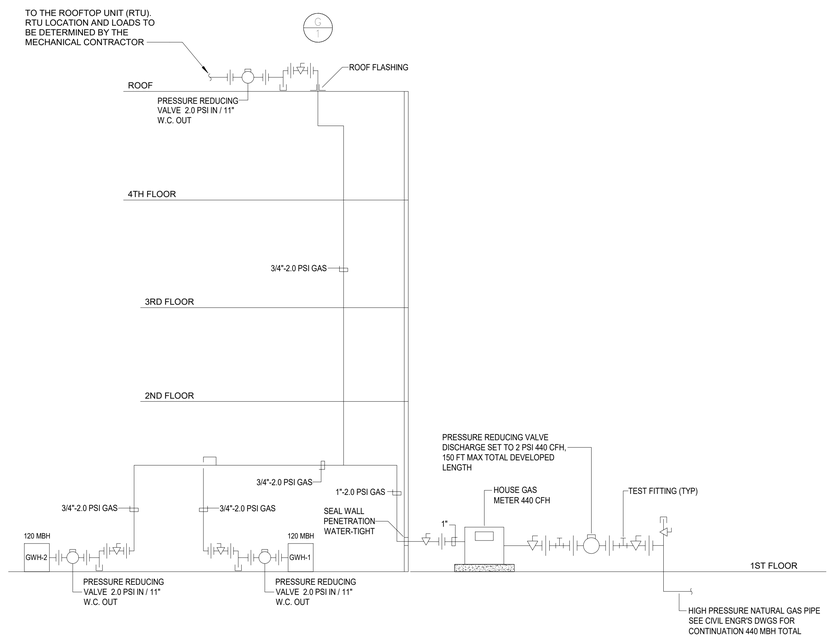

2 APARTMENT BLDG - GAS RISER DIAGRAM

NTS

REVISION	DESCRIPTION	BY	DATE

ARCHITECT

MEP. ENG.

NIST

FOR OFFICIAL USE ONLY

U.S. DEPARTMENT OF COMMERCE

OFFICE OF FACILITIES & PROPERTY MANAGEMENT

NIST – MID RISE APARTMENT


PLUMBING RISERS


P502

SH. NO. ___ OF ___

DWG. P502

APPROVED BY	DATE	SPONSOR	DATE	MAINTENANCE ENG. OFF.	DATE	ENVIRONMENTAL MANAGEMENT	DATE	SAFETY	DATE	SHED – NIST FIRE MARSHAL/AHJ	DATE	FACILITIES ENGR. OFF.	DATE	PROJECT LEADER	DATE	DRAWN BY	DATE	PROJECT/ W.O. #
														VAY		AA	08/15/2022	Project Number

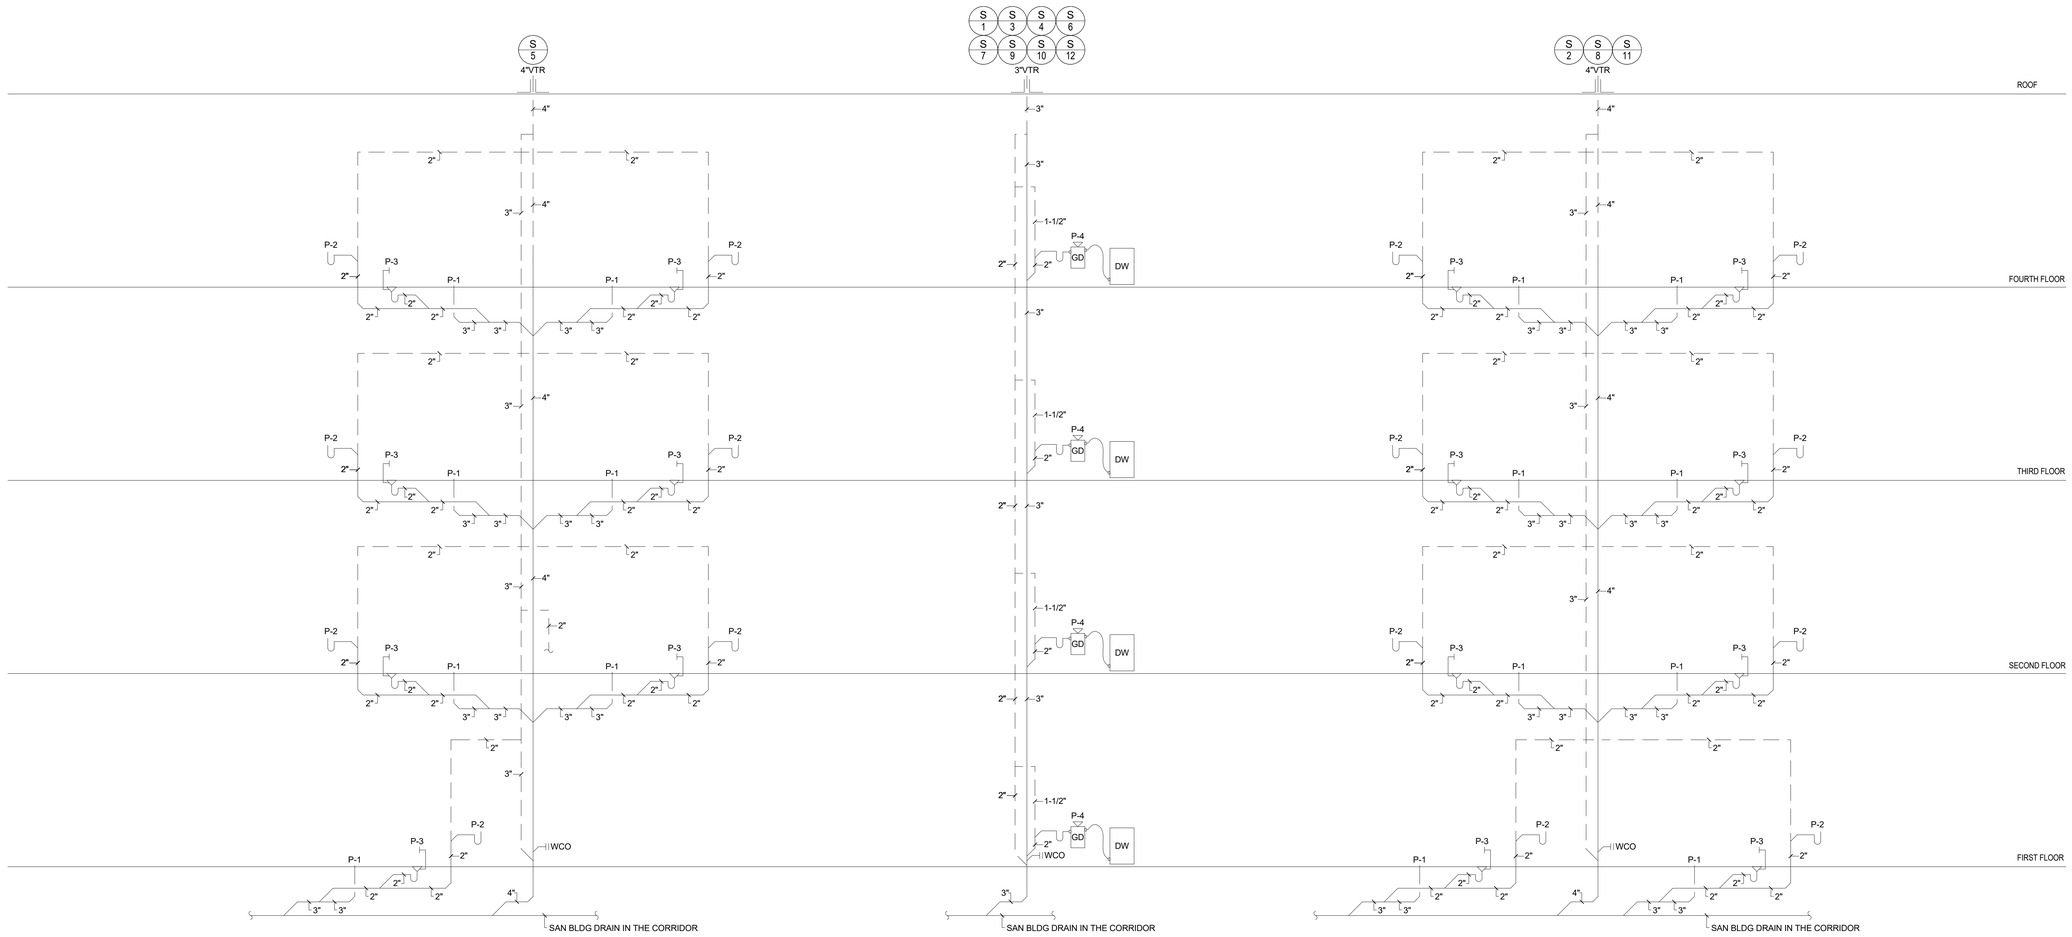

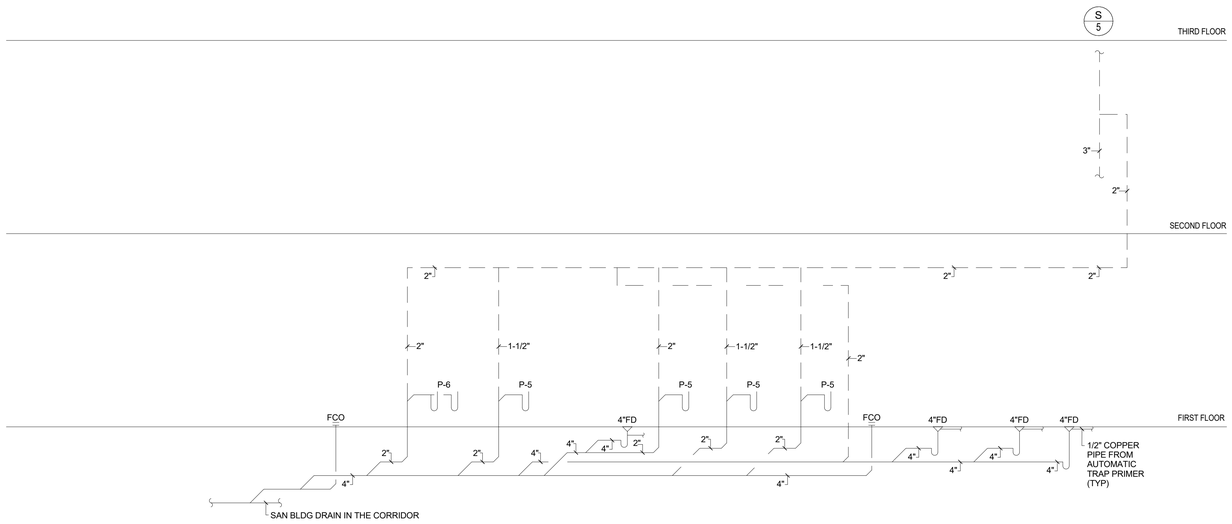

1 APARTMENT BLDG - SANITARY RISER DIAGRAM

NTS

REVISION	DESCRIPTION	BY	DATE

ARCHITECT

MEP. ENG.

NIST

FOR OFFICIAL USE ONLY

U.S. DEPARTMENT OF COMMERCE

OFFICE OF FACILITIES & PROPERTY MANAGEMENT

NIST – MID RISE APARTMENT

PLUMBING RISERS

P503

SH. NO. ___ OF ___

DWG. P503

APPROVED BY	DATE	SPONSOR	DATE	MAINTENANCE ENG. OFF.	DATE	ENVIRONMENTAL MANAGEMENT	DATE	SAFETY	DATE	SHED – NIST FIRE MARSHAL/AHJ	DATE	FACILITIES ENGR. OFF.	DATE	PROJECT LEADER	DATE	DRAWN BY	DATE	PROJECT/ W.O. #
														VAY		AA	08/15/2022	Project Number